

**PRICE SCOPE: only the Nudura ICF formwork and associated accessories are included in our price.**
All other structure and information shown is supplied in good faith for coordination only and must be checked by the relevant professional.

**QUOTATION - NOT FOR CONSTRUCTION**


## J1 - 6,125 O/A x 253 deep - 38 No.

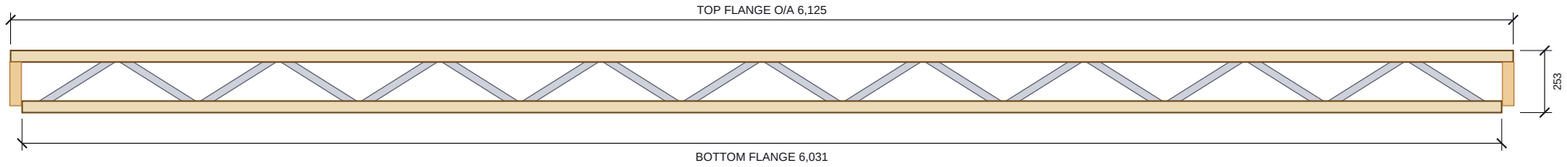



## J2 - 2,913 O/A x 253 deep - 14 No.

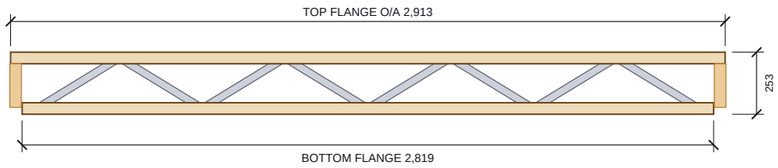


## J3 - 1,538 O/A x 253 deep - 6 No.

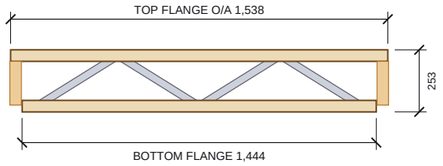


Elevations 1:25 (ledgers at each end shown for context)

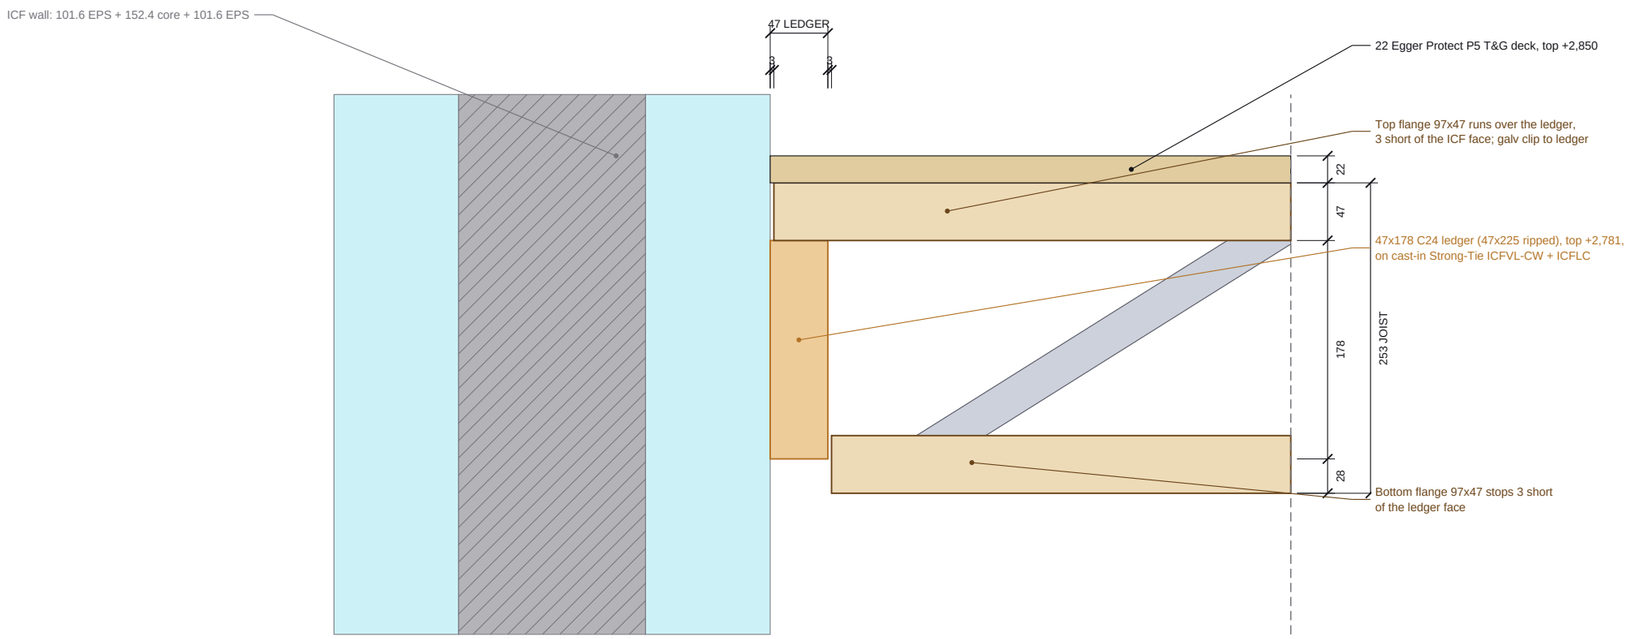


## TOP-HUNG BEARING ON CUT-DOWN LEDGER

Scale 1:5 | typical, both ends of every joist

## JOIST TYPES

### JOIST SCHEDULE

| Type | O/A | Bottom | Depth | Flanges | Qty |
|---|---|---|---|---|---|
| J1 | 6,125 | 6,031 | 253 | 97x47 | 38 |
| J2 | 2,913 | 2,819 | 253 | 97x47 | 14 |
| J3 | 1,538 | 1,444 | 253 | 97x47 | 6 |
| | | | | **Total** | **58** |

Qty = both flats (A/B + C/D). PS10 equivalent, for supplier quote.

### WHERE USED

| Type | Location |
|---|---|
| J1 | Main span front-to-rear wall, both flats (clear 6,131) |
| J2 | Rear, stair-enclosure wall to the rear wall |
| J3 | Front, beside the stair well, to the stair-enclosure wall |

### NOTES

1. FOR SUPPLIER QUOTE: 253 deep metal-web joists, e.g. Posi-Joist / Easi-Joist PS10 equivalent, 97 x 47 C24 (or stress-graded) flanges with galvanised V-web plates. The supplier designs the joists for the stated loads and confirms depth, web layout and spacing.
2. Loads (to be confirmed by the supplier): domestic floor, imposed 1.5 kN/m2 + lightweight stud partitions over, 22 Egger Protect P5 deck, plasterboard ceiling under. 400 c/c.
3. Top-hung bearing at both ends: top flange runs over the 47 x 178 C24 ledger to 3 short of the ICF face; bottom flange stops 3 short of the ledger. Galv top-chord restraint clip nailed to the ledger at each end.
4. Web pattern shown is indicative (from the quotation model); webs at the supplier's standard pitch.

### REVISIONS

| REV | DATE | DESCRIPTION |
|---|---|---|
| Q01 | 16.10.26 | First issue |

Nudura™ BuildEase

| CLIENT | PROJECT |
|---|---|
| Beech Developments | Lon Eilian, Caernarfon |

DRAWING TITLE
**FLOOR JOIST PROFILES**
Metal-web joist profiles for supplier quotation

| SCALE | SIZE | DATE |
|---|---|---|
| 1:25 / 1:5 | A3 | 16.10.26 |
| DRAWN | CHECKED | APPROVED |
| TS | | |

| STATUS | DRAWING No. | REV |
|---|---|---|
| QUOTATION | ES26-081-FL-02 | Q01 |

Do not scale. All dimensions in mm. Check all dimensions on site.