
PRICE SCOPE: only the Nudura ICF formwork and associated accessories are included in our price. All other structure and information shown is supplied in good faith for coordination only and must be checked by the relevant professional.

QUOTATION - NOT FOR CONSTRUCTION

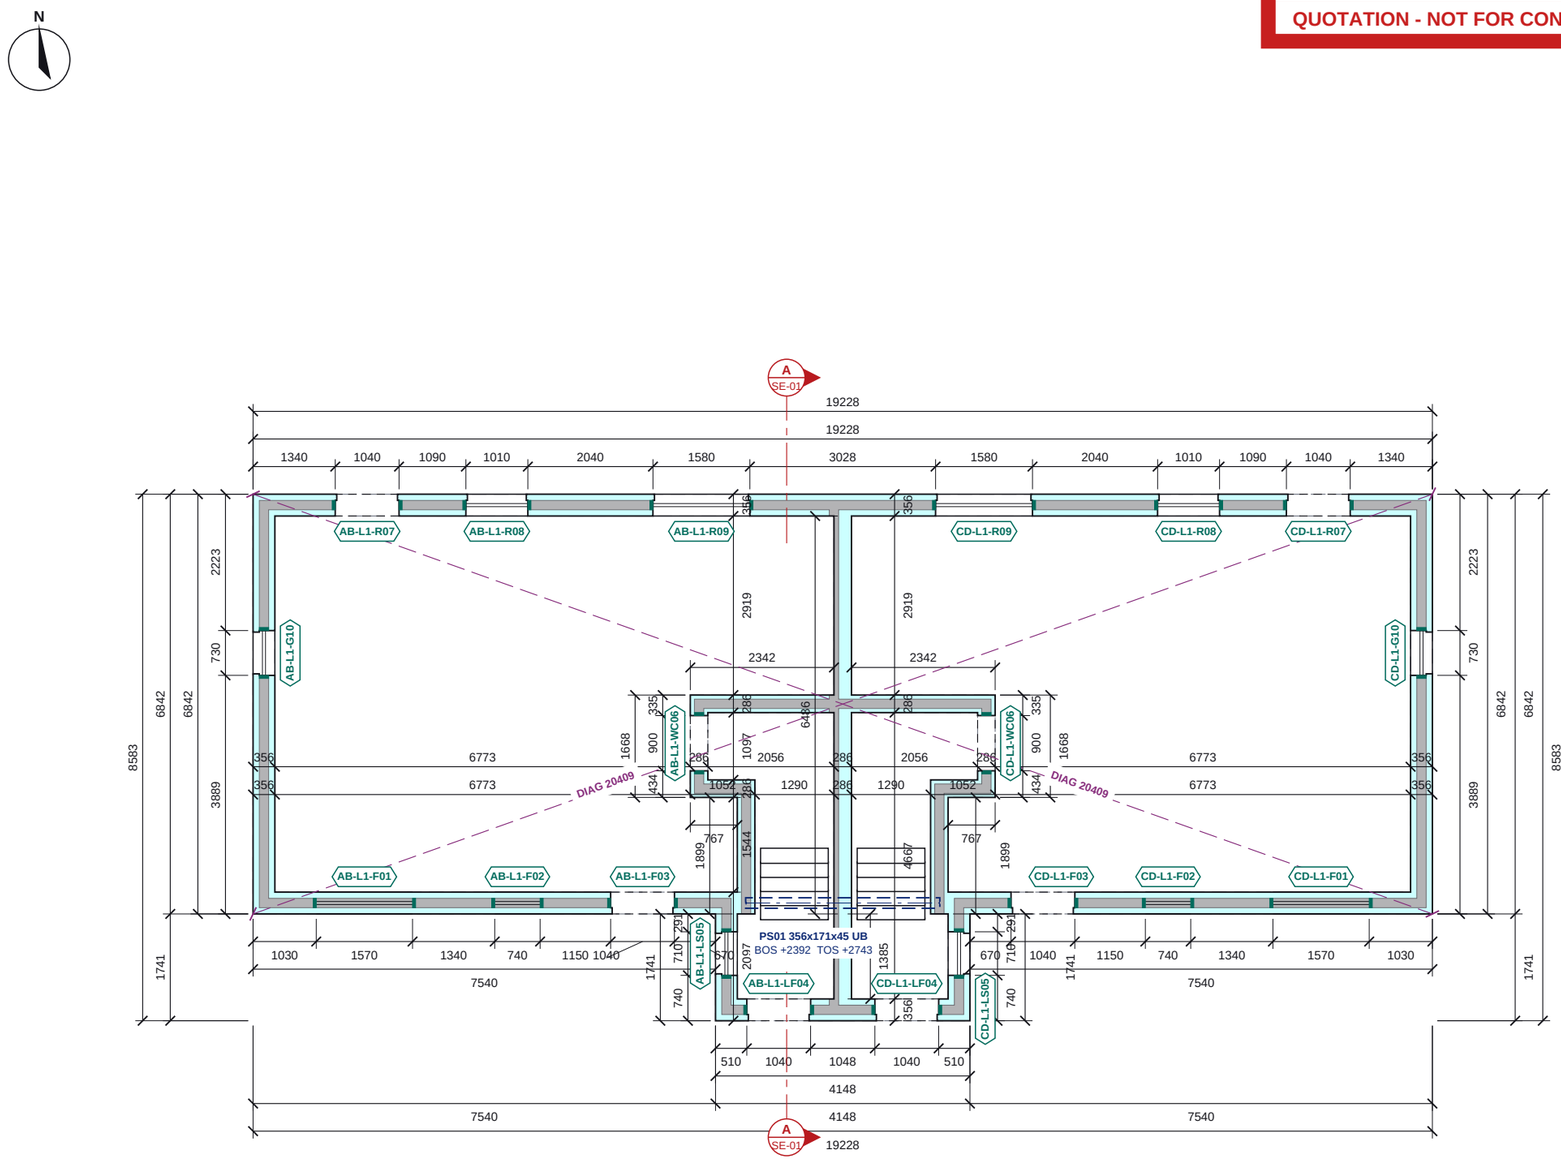

EPS insulation (Nudura form)
Concrete core
End cap at opening
ICF walls of the level below (dashed)
Steel over (dashed), marked
Engineer's pier bars (n-H12 vertical bars in ICF pier) / WS wall starters
Setting-out check diagonal (external ICF corners)
Section line (see SE sheet)

GROUND FLOOR ICF PLAN

Scale 1:100 @ A3 | Plan cut at +900

0 1 2 3 4 5m

GROUND FLOOR ICF SCHEDULES

OPENING SCHEDULE

Ref	Width	Height	Sill	Head	Lintel
AB-L1-F01	1570	1000	+1100	+2100	-
AB-L1-F02	740	1000	+1100	+2100	-
AB-L1-F03	1040	2100	0	+2100	-
AB-L1-G10	730	1300	+800	+2100	-
AB-L1-LF04	1040	2100	0	+2100	-
AB-L1-LS05	710	1300	+800	+2100	-
AB-L1-R07	1040	2100	0	+2100	-
AB-L1-R08	1010	1300	+800	+2100	-
AB-L1-R09	1580	1300	+800	+2100	-
AB-L1-WC06	900	2100	0	+2100	-
CD-L1-F01	1570	1000	+1100	+2100	-
CD-L1-F02	740	1000	+1100	+2100	-
CD-L1-F03	1040	2100	0	+2100	-
CD-L1-G10	730	1300	+800	+2100	-
CD-L1-LF04	1040	2100	0	+2100	-
CD-L1-LS05	710	1300	+800	+2100	-
CD-L1-R07	1040	2100	0	+2100	-
CD-L1-R08	1010	1300	+800	+2100	-
CD-L1-R09	1580	1300	+800	+2100	-
CD-L1-WC06	900	2100	0	+2100	-

Structural openings in the ICF; sill and head above GF FFL.

STEEL SCHEDULE

Mark	Section (engineer)	BOS	TOS
PS01	356x171x45 UB S355	+2392	+2743

BOS / TOS = bottom / top of steel above GF FFL (C-1 columns: base / top).

NOTES

1. ICF: Nudura 6" XR35, 101.6 EPS + 152.4 core + 101.6 EPS = 355.6; 6" Std, 66.7 EPS + 152.4 core + 66.7 EPS = 285.8. Dimensions to the ICF faces.
2. Levels above GF FFL. Sill / head = structural opening in the ICF.
3. No structural design exists yet. ICF per the quotation model: 6in XR35 external walls, 6in Standard party and stair-enclosure walls. The porch steel (UKB 356x171x45 S355 under the first-floor front wall) is TLS-proposed for the engineer's review.
4. Lintel (L-n) and steel (B-n, C-1) marks from rev -, which takes precedence.
5. Masonry walls shown for context.
6. Steel over dashed. BOS / TOS = bottom / top of steel above GF FFL.

REVISIONS

REV	DATE	DESCRIPTION
Q01	16.10.26	First issue

Nudura™ BuildEase

CLIENT	PROJECT
Beech Developments	Lon Eilian, Caernarfon

DRAWING TITLE

GROUND FLOOR ICF GENERAL ARRANGEMENT

ICF walls, openings, lintels, steel over and engineer's notes

SCALE	SIZE	DATE
1:100	A3	16.10.26
DRAWN	CHECKED	APPROVED
TS		

STATUS	DRAWING No.	REV
QUOTATION	ES26-081-GA-02	Q01

Do not scale. All dimensions in millimetres, levels in metres from GF FFL. Check all dimensions on site.