

QUOTATION - NOT FOR CONSTRUCTION

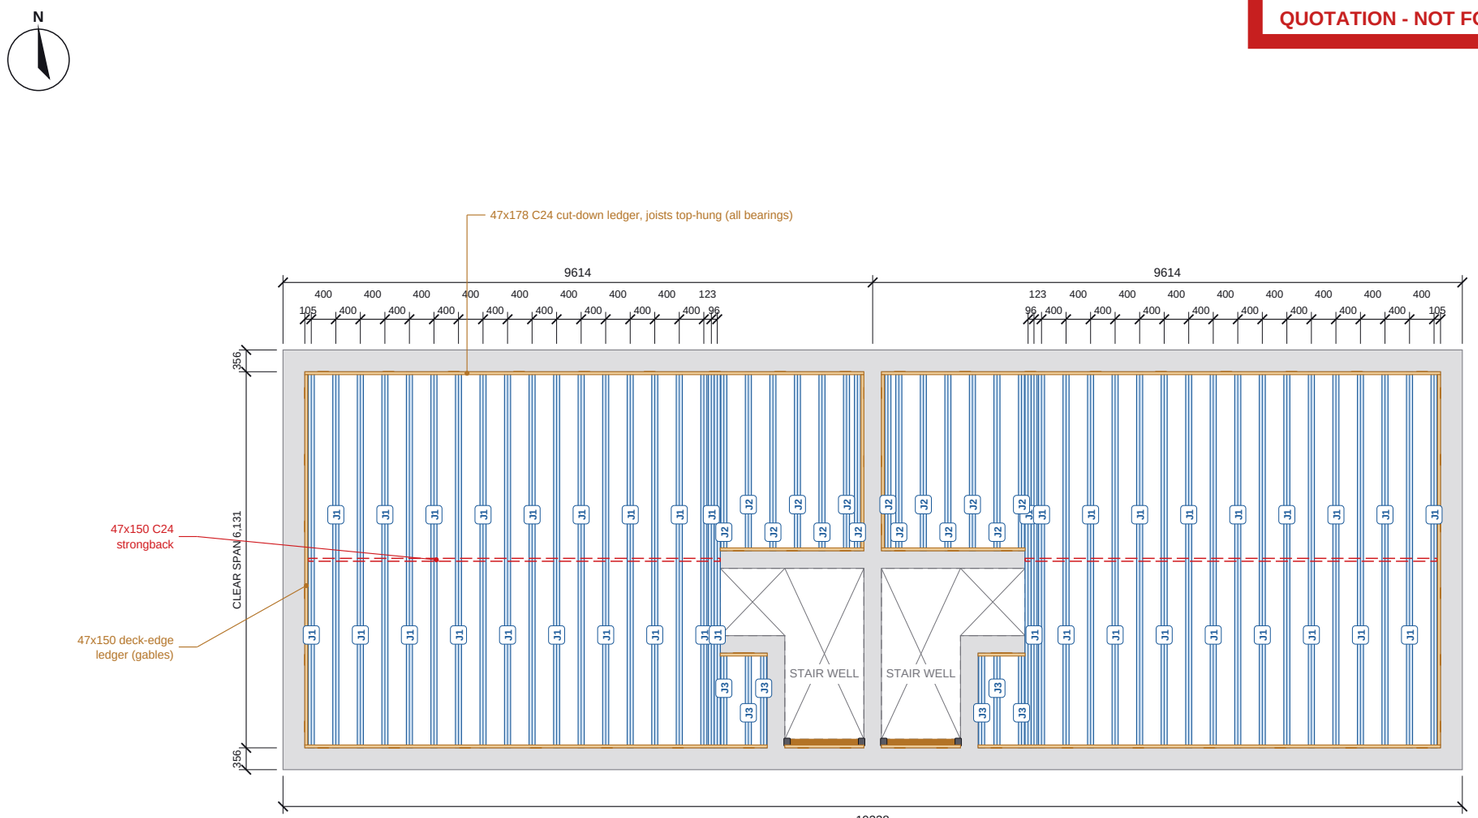

Stair well framing: see enlarged plan


FIRST FLOOR JOIST LAYOUT

Scale 1:100 @ A3 | Plan on the FF joists, deck omitted

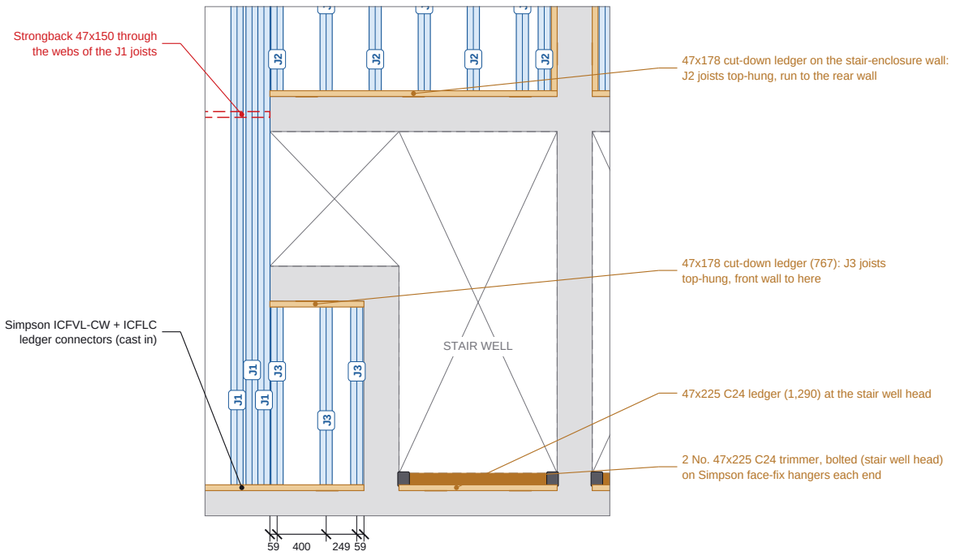

STAIR WELL FRAMING A/B - ENLARGED

Scale 1:50 | C/D handed (mirror)

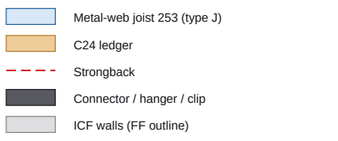



Do not scale. All dimensions in mm. Check all dimensions on site.

FIRST FLOOR SCHEDULES

JOIST SCHEDULE (253 DEEP, @400)

Type	O/A	Bottom	A/B	C/D	Total
J1	6,125	6,031	19	19	38
J2	2,913	2,819	7	7	14
J3	1,538	1,444	3	3	6
	Total		**29**	**29**	**58**

O/A = top flange overall length; Bottom = bottom flange length. Profiles on ES26-081-FL-02.

LEDGERS, STRONGBACKS, TRIMMERS (C24)

Item	Length	Qty
2 No. 47x225 trimmer, bolted	1,284	2
47x150 deck-edge ledger	6,037	2
47x150 deck-edge ledger	2,825	2
47x150 strongback	6,716	2
47x178 ledger cut-down ledger	9,116	2
47x178 ledger cut-down ledger	7,540	2
47x178 ledger cut-down ledger	2,342	2
47x178 ledger cut-down ledger	767	2
47x225 ledger	1,290	2

METALWORK AND DECK

Item	Qty
22 Egger Protect P5 T&G board	92
Face-fix trimmer hanger	4
Strong-Tie ICFVL-CW + ICFLC connector	64
Top-chord restraint clip (galv)	116

NOTES

1. First floor: 253 deep metal-web joists (PS10 / Posi-Joist / Easi-Joist equivalent, 97 x 47 C24 flanges) at 400 c/c, TOP-HUNG: the top flange runs over a 47 x 178 C24 ledger (47 x 225 ripped down) and stops 3 short of the ICF face; the bottom flange stops 3 short of the ledger. Galv restraint clip at every bearing.
2. Ledgers fixed to the ICF with cast-in Simpson Strong-Tie ICFVL-CW + ICFLC connectors (spacing to the connector manufacturer's table). Top of ledger +2,781, top of joists +2,828 above GF FFL.
3. Deck: 22 Egger Protect P5 T&G, glued and screwed to every joist, laid across the joists.
4. 47 x 150 C24 strongback through the webs at mid-span of the long joists, fixed to the vertical web plates. Stair well head: 2 No. 47 x 225 C24 trimmer bolted, on face-fix hangers.
5. Joist supplier to design and confirm joist depth, spacing, bracing and ledger fixings; layout for pricing only.

REVISIONS

REV	DATE	DESCRIPTION
Q01	16.10.26	First issue

Nudura™ BuildEase

CLIENT	PROJECT
Beech Developments	Lon Eilian, Caernarfon

DRAWING TITLE

FIRST FLOOR LAYOUT

Metal-web joists, ledgers, strongbacks, stair well trimmers

SCALE	SIZE	DATE
1:100	A3	16.10.26
DRAWN	CHECKED	APPROVED
TS		

STATUS	DRAWING No.	REV
QUOTATION	ES26-081-FL-01	Q01