

QUOTATION - NOT FOR CONSTRUCTION


J1 - 6,125 O/A x 253 deep - 38 No.

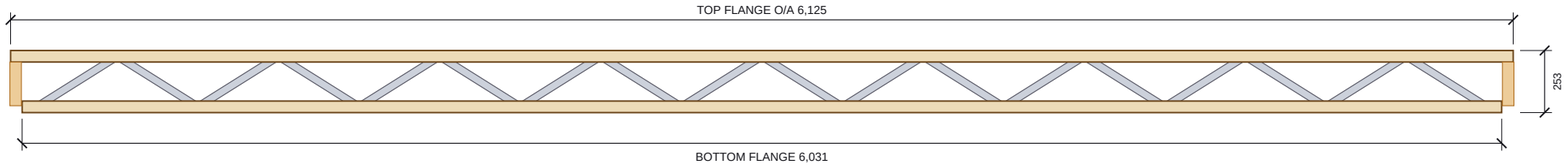


J2 - 2,913 O/A x 253 deep - 14 No.

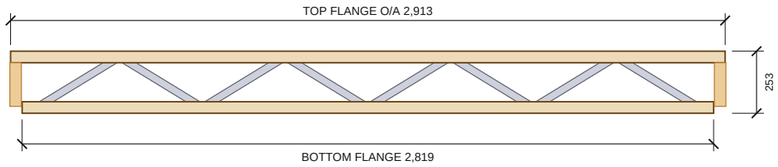

J3 - 1,538 O/A x 253 deep - 6 No.

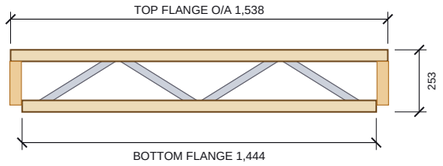

Elevations 1:25 (ledgers at each end shown for context)

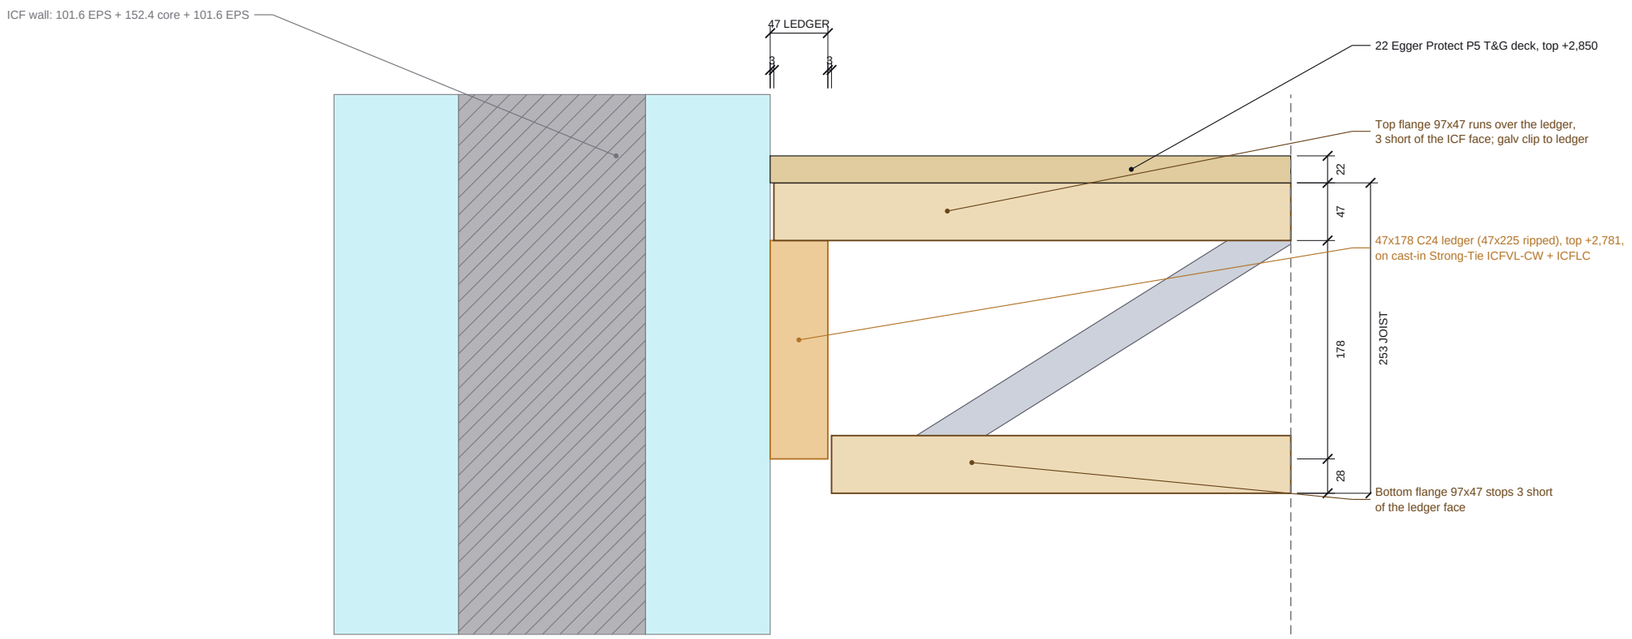

TOP-HUNG BEARING ON CUT-DOWN LEDGER

Scale 1:5 | typical, both ends of every joist

JOIST TYPES

JOIST SCHEDULE

Type	O/A	Bottom	Depth	Flanges	Qty
J1	6,125	6,031	253	97x47	38
J2	2,913	2,819	253	97x47	14
J3	1,538	1,444	253	97x47	6
				Total	**58**

Qty = both flats (A/B + C/D). PS10 equivalent, for supplier quote.

WHERE USED

Type	Location
J1	Main span front-to-rear wall, both flats (clear 6,131)
J2	Rear, stair-enclosure wall to the rear wall
J3	Front, beside the stair well, to the stair-enclosure wall

NOTES

1. FOR SUPPLIER QUOTE: 253 deep metal-web joists, e.g. Posi-Joist / Easi-Joist PS10 equivalent, 97 x 47 C24 (or stress-graded) flanges with galvanised V-web plates. The supplier designs the joists for the stated loads and confirms depth, web layout and spacing.
2. Loads (to be confirmed by the supplier): domestic floor, imposed 1.5 kN/m2 + lightweight stud partitions over, 22 Egger Protect P5 deck, plasterboard ceiling under. 400 c/c.
3. Top-hung bearing at both ends: top flange runs over the 47 x 178 C24 ledger to 3 short of the ICF face; bottom flange stops 3 short of the ledger. Galv top-chord restraint clip nailed to the ledger at each end.
4. Web pattern shown is indicative (from the quotation model); webs at the supplier's standard pitch.

REVISIONS

REV	DATE	DESCRIPTION
Q01	16.10.26	First issue

Nudura™ BuildEase

CLIENT	PROJECT
Beech Developments	Lon Eilian, Caernarfon

DRAWING TITLE

FLOOR JOIST PROFILES

Metal-web joist profiles for supplier quotation

SCALE	SIZE	DATE
1:25 / 1:5	A3	16.10.26
DRAWN	CHECKED	APPROVED
TS		

STATUS	DRAWING No.	REV
QUOTATION	ES26-081-FL-02	Q01

Do not scale. All dimensions in mm. Check all dimensions on site.