
QUOTATION - NOT FOR CONSTRUCTION

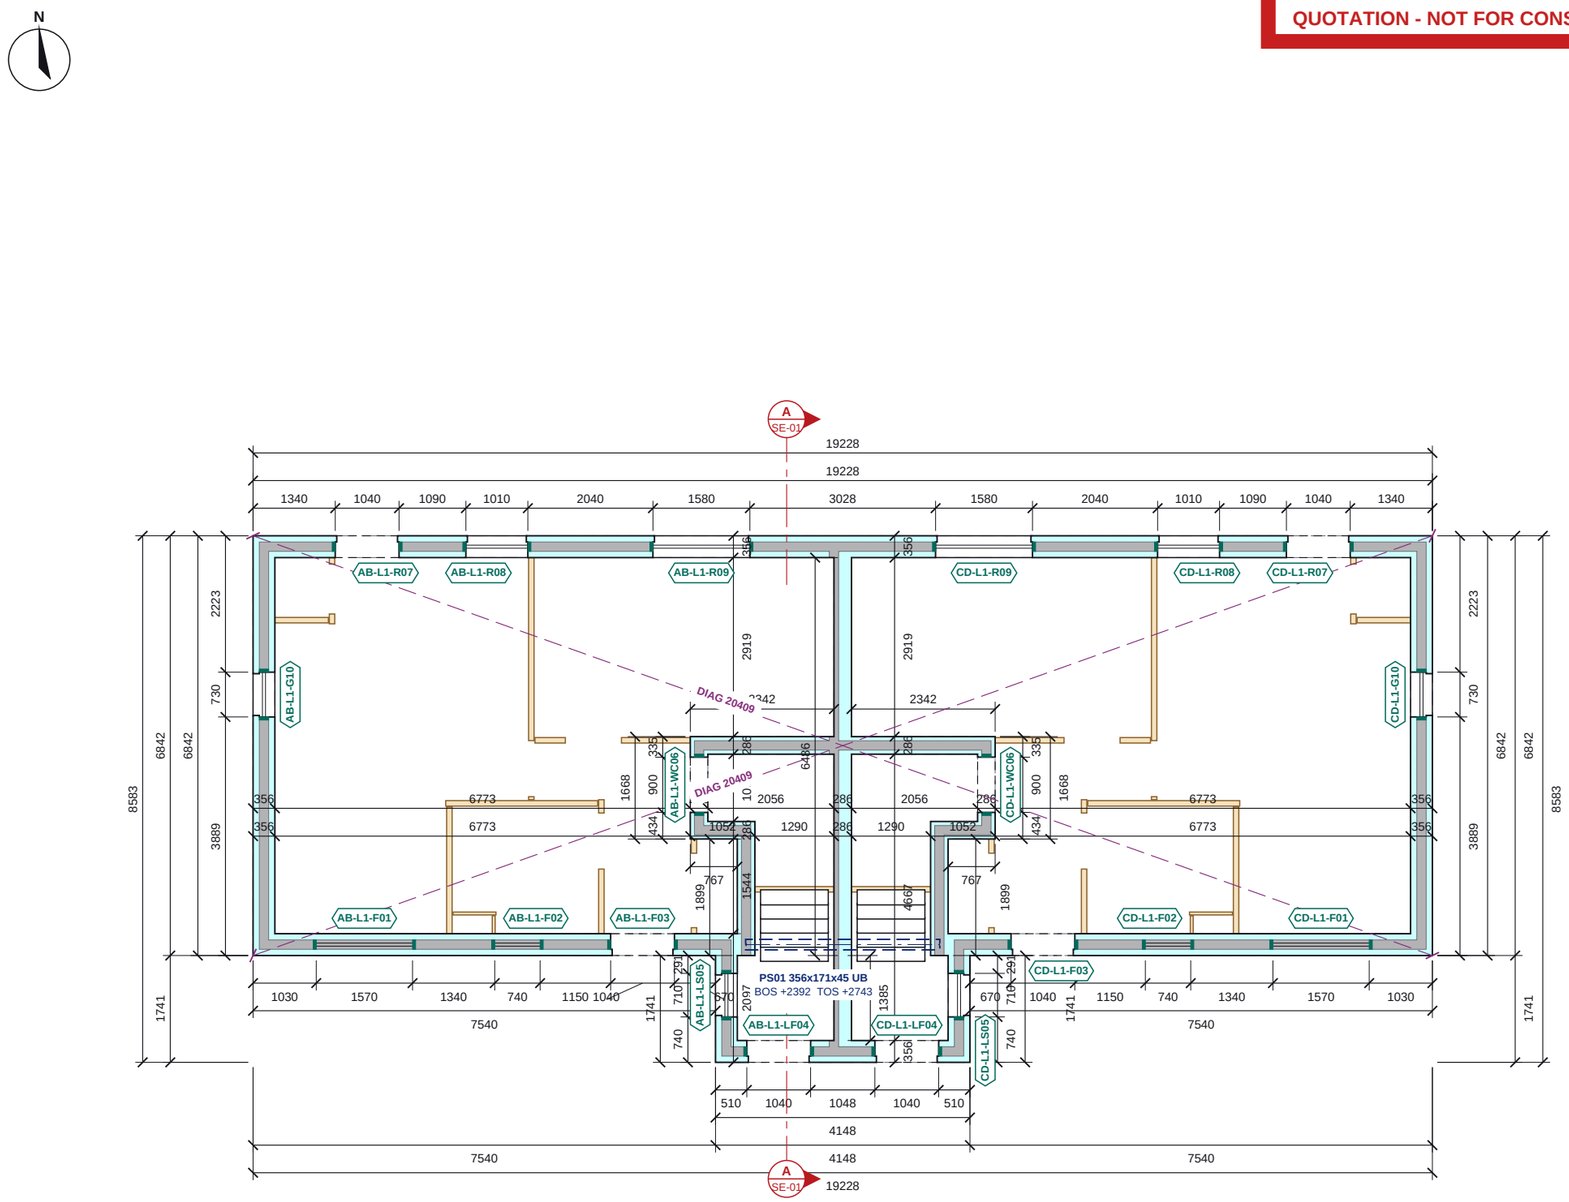

EPS insulation (Nudura form)
Concrete core
End cap at opening
Timber stud partition (internal, non-loadbearing)
ICF walls of the level below (dashed)
Steel over (dashed), marked
Engineer's pier bars (n-H12 vertical bars in ICF pier) / WS wall starters
Setting-out check diagonal (external ICF corners)
Section line (see SE sheet)

GROUND FLOOR ICF PLAN

Scale 1:100 @ A3 | Plan cut at +900

0 1 2 3 4 5m

Do not scale. All dimensions in millimetres; levels in metres from GF FFL. Check all dimensions on site.

GROUND FLOOR ICF SCHEDULES

OPENING SCHEDULE

Ref	Width	Height	Sill	Head	Lintel
AB-L1-F01	1570	1000	+1100	+2100	-
AB-L1-F02	740	1000	+1100	+2100	-
AB-L1-F03	1040	2100	0	+2100	-
AB-L1-G10	730	1300	+800	+2100	-
AB-L1-LF04	1040	2100	0	+2100	-
AB-L1-LS05	710	1300	+800	+2100	-
AB-L1-R07	1040	2100	0	+2100	-
AB-L1-R08	1010	1300	+800	+2100	-
AB-L1-R09	1580	1300	+800	+2100	-
AB-L1-WC06	900	2100	0	+2100	-
CD-L1-F01	1570	1000	+1100	+2100	-
CD-L1-F02	740	1000	+1100	+2100	-
CD-L1-F03	1040	2100	0	+2100	-
CD-L1-G10	730	1300	+800	+2100	-
CD-L1-LF04	1040	2100	0	+2100	-
CD-L1-LS05	710	1300	+800	+2100	-
CD-L1-R07	1040	2100	0	+2100	-
CD-L1-R08	1010	1300	+800	+2100	-
CD-L1-R09	1580	1300	+800	+2100	-
CD-L1-WC06	900	2100	0	+2100	-

Structural openings in the ICF; sill and head above GF FFL.

STEEL SCHEDULE

Mark	Section (engineer)	BOS	TOS
PS01	356x171x45 UB S355	+2392	+2743

BOS / TOS = bottom / top of steel above GF FFL (C-1 columns: base / top).

NOTES

1. ICF: Nudura 6" XR35, 101.6 EPS + 152.4 core + 101.6 EPS = 355.6; 6" Std, 66.7 EPS + 152.4 core + 66.7 EPS = 285.8. Dimensions to the ICF faces.
2. Levels above GF FFL. Sill / head = structural opening in the ICF.
3. No structural design exists yet. ICF per the quotation model: 6in XR35 external walls, 6in Standard party and stair-enclosure walls. The porch steel (UKB 356x171x45 S355 under the first-floor front wall) is TLS-proposed for the engineer's review.
4. Lintel (L-n) and steel (B-n, C-1) marks from rev -, which takes precedence.
5. Masonry walls shown for context.
6. Steel over dashed. BOS / TOS = bottom / top of steel above GF FFL.

REVISIONS

REV	DATE	DESCRIPTION
Q01	16.10.26	First issue

Nudura™ BuildEase

CLIENT	PROJECT
Beech Developments	Lon Eilian, Caernarfon

DRAWING TITLE

GROUND FLOOR ICF GENERAL ARRANGEMENT

ICF walls, openings, lintels, steel over and engineer's notes

SCALE	SIZE	DATE
1:100	A3	16.10.26
DRAWN	CHECKED	APPROVED
TS		

STATUS	DRAWING No.	REV
QUOTATION	ES26-081-GA-02	Q01