

QUOTATION - NOT FOR CONSTRUCTION

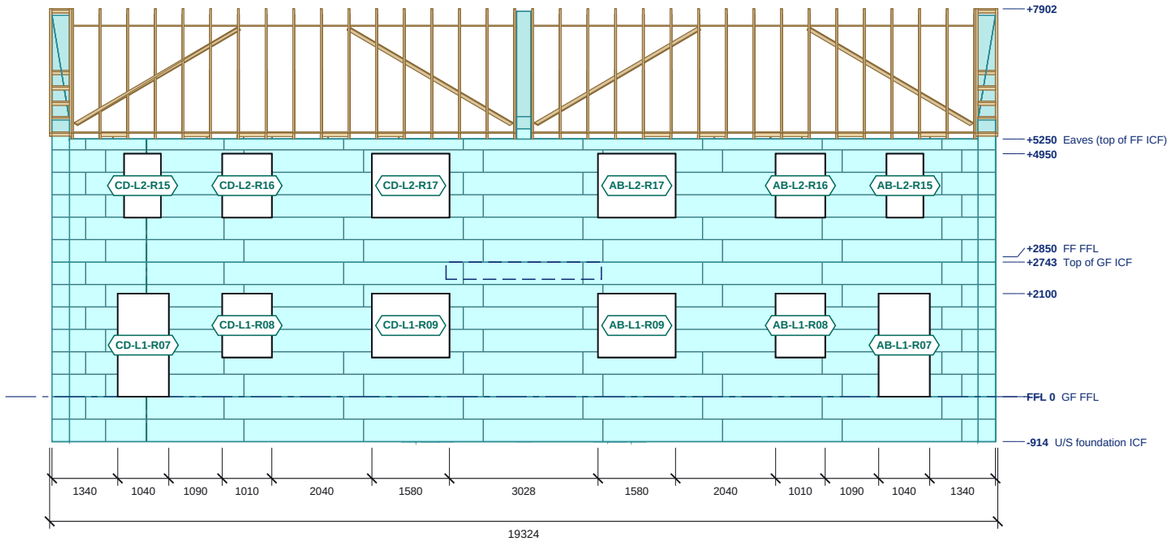

NORTH ELEVATION

Scale 1:125 @ A3 | Levels above GF FFL; sills and heads in the schedule

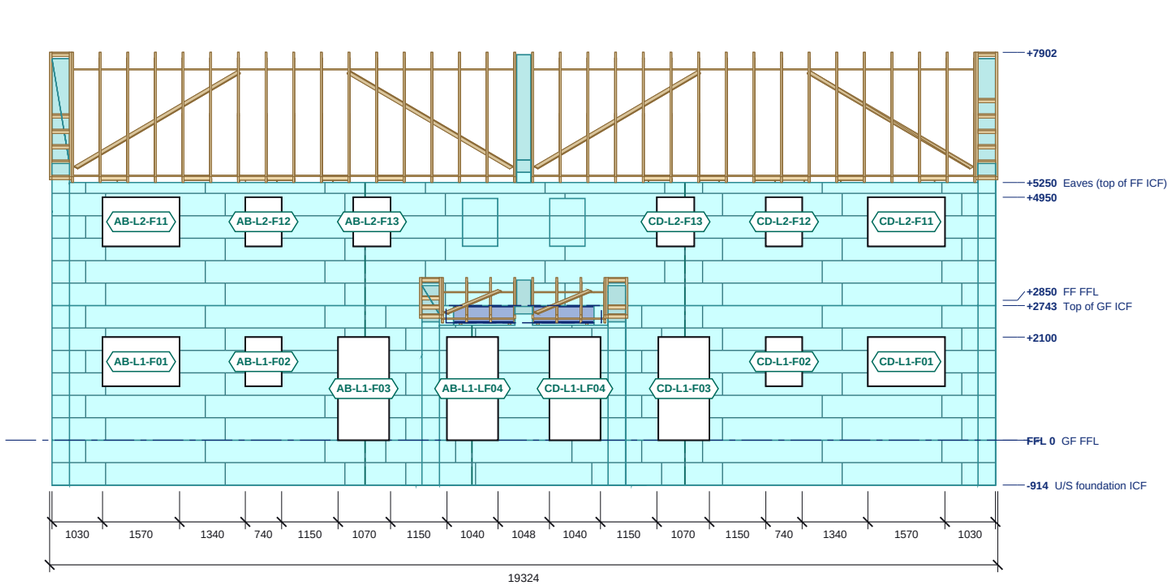

SOUTH ELEVATION

Scale 1:125 @ A3 | Levels above GF FFL; sills and heads in the schedule

ICF external EPS face
Block course joint
Stack joint
Steel

0 1 2 3 4 5m

Do not scale. All dimensions in millimetres, levels in metres from GF FFL. Check all dimensions on site.

ELEVATION SCHEDULES

NORTH ELEVATION: OPENINGS

Ref	Width	Height	Sill	Head	Lintel
AB-L1-R07	1040	2100	0	+2100	-
AB-L1-R08	1010	1300	+800	+2100	-
AB-L1-R09	1580	1300	+800	+2100	-
AB-L2-R15	750	1300	+3650	+4950	-
AB-L2-R16	1010	1300	+3650	+4950	-
AB-L2-R17	1580	1300	+3650	+4950	-
CD-L1-R07	1040	2100	0	+2100	-
CD-L1-R08	1010	1300	+800	+2100	-
CD-L1-R09	1580	1300	+800	+2100	-
CD-L2-R15	750	1300	+3650	+4950	-
CD-L2-R16	1010	1300	+3650	+4950	-
CD-L2-R17	1580	1300	+3650	+4950	-

Structural openings in the ICF; sill and head above GF FFL.

SOUTH ELEVATION: OPENINGS

Ref	Width	Height	Sill	Head	Lintel
AB-L1-F01	1570	1000	+1100	+2100	-
AB-L1-F02	740	1000	+1100	+2100	-
AB-L1-F03	1040	2100	0	+2100	-
AB-L1-LF04	1040	2100	0	+2100	-
AB-L2-F11	1570	1000	+3950	+4950	-
AB-L2-F12	740	1000	+3950	+4950	-
AB-L2-F13	760	1000	+3950	+4950	-
CD-L1-F01	1570	1000	+1100	+2100	-
CD-L1-F02	740	1000	+1100	+2100	-
CD-L1-F03	1040	2100	0	+2100	-
CD-L1-LF04	1040	2100	0	+2100	-
CD-L2-F11	1570	1000	+3950	+4950	-
CD-L2-F12	740	1000	+3950	+4950	-
CD-L2-F13	760	1000	+3950	+4950	-

Structural openings in the ICF; sill and head above GF FFL.

LEVELS ON THESE ELEVATIONS

Level	FFL
U/S foundation ICF	-914
GF FFL	0
top of ICF	+2100
Top of GF ICF	+2743
FF FFL	+2850
top of ICF	+4950
Eaves (top of FF ICF)	+5250
top of roof build-up	+7902

NOTES

1. ICF: Nudura 6" XR35, 101.6 EPS + 152.4 core + 101.6 EPS = 355.6; 6" Std, 66.7 EPS + 152.4 core + 66.7 EPS = 285.8. External EPS face shown with the block course joints, vertical block joints and stack joints as populated.
2. Levels above GF FFL. Openings are structural openings in the ICF; glazing, doors, render and finishes by others, not shown.
3. Steel shown as modelled.
4. See ES26-081-GA-01 for plan setting out, lintels and steel.

REVISIONS

REV	DATE	DESCRIPTION
Q01	16.10.26	First issue

Nudura™ BuildEase

CLIENT	PROJECT
Beech Developments	Lon Eilian, Caernarfon

DRAWING TITLE

NORTH AND SOUTH ELEVATIONS

ICF elevations with openings, levels and roof build-up

SCALE	SIZE	DATE
1:125	A3	16.10.26
DRAWN	CHECKED	APPROVED
TS		

STATUS	DRAWING No.	REV
QUOTATION	ES26-081-EL-01	Q01