
QUOTATION - NOT FOR CONSTRUCTION

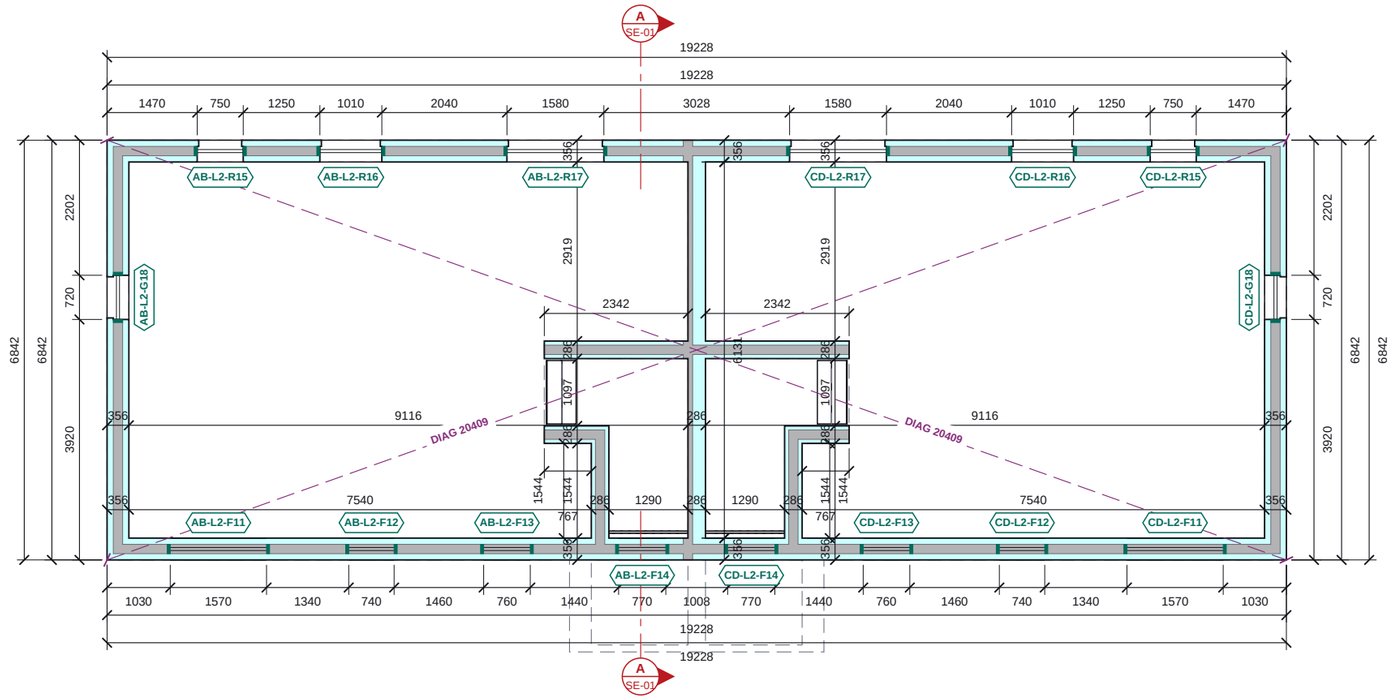

- EPS insulation (Nudura form)
- Concrete core
- End cap at opening
- ICF walls of the level below (dashed)
- Engineer's pier bars (n-H12 vertical bars in ICF pier) / WS wall starters
- Setting-out check diagonal (external ICF corners)
- Section line (see SE sheet)

FIRST FLOOR ICF PLAN

Scale 1:100 @ A3 | Plan cut at +3943

0 1 2 3 4 5m

FIRST FLOOR ICF SCHEDULES

OPENING SCHEDULE

Ref	Width	Height	Sill	Head	Lintel
AB-L2-F11	1570	1000	+3950	+4950	-
AB-L2-F12	740	1000	+3950	+4950	-
AB-L2-F13	760	1000	+3950	+4950	-
AB-L2-F14	770	1000	+3950	+4950	-
AB-L2-G18	720	1300	+3650	+4950	-
AB-L2-R15	750	1300	+3650	+4950	-
AB-L2-R16	1010	1300	+3650	+4950	-
AB-L2-R17	1580	1300	+3650	+4950	-
CD-L2-F11	1570	1000	+3950	+4950	-
CD-L2-F12	740	1000	+3950	+4950	-
CD-L2-F13	760	1000	+3950	+4950	-
CD-L2-F14	770	1000	+3950	+4950	-
CD-L2-G18	720	1300	+3650	+4950	-
CD-L2-R15	750	1300	+3650	+4950	-
CD-L2-R16	1010	1300	+3650	+4950	-
CD-L2-R17	1580	1300	+3650	+4950	-

Structural openings in the ICF; sill and head above GF FFL.

NOTES

1. ICF: Nudura 6" XR35, 101.6 EPS + 152.4 core + 101.6 EPS = 355.6; 6" Std, 66.7 EPS + 152.4 core + 66.7 EPS = 285.8. Dimensions to the ICF faces.
2. Levels above GF FFL. Sill / head = structural opening in the ICF.
3. No structural design exists yet. ICF per the quotation model: 6in XR35 external walls, 6in Standard party and stair-enclosure walls. The porch steel (UKB 356x171x45 S355 under the first-floor front wall) is TLS-proposed for the engineer's review.
4. Lintel (L-n) and steel (B-n, C-1) marks from rev -, which takes precedence.
5. Masonry walls shown for context.

REVISIONS

REV	DATE	DESCRIPTION
Q01	16.10.26	First issue

Nudura™ BuildEase

CLIENT	PROJECT
Beech Developments	Lon Eilian, Caernarfon

DRAWING TITLE

FIRST FLOOR ICF GENERAL ARRANGEMENT

ICF walls, openings, lintels, steel over and engineer's notes

SCALE	SIZE	DATE
1:100	A3	16.10.26
DRAWN	CHECKED	APPROVED
TS		

STATUS	DRAWING No.	REV
QUOTATION	ES26-081-GA-03	Q01

Do not scale. All dimensions in millimetres, levels in metres from GF FFL. Check all dimensions on site.